


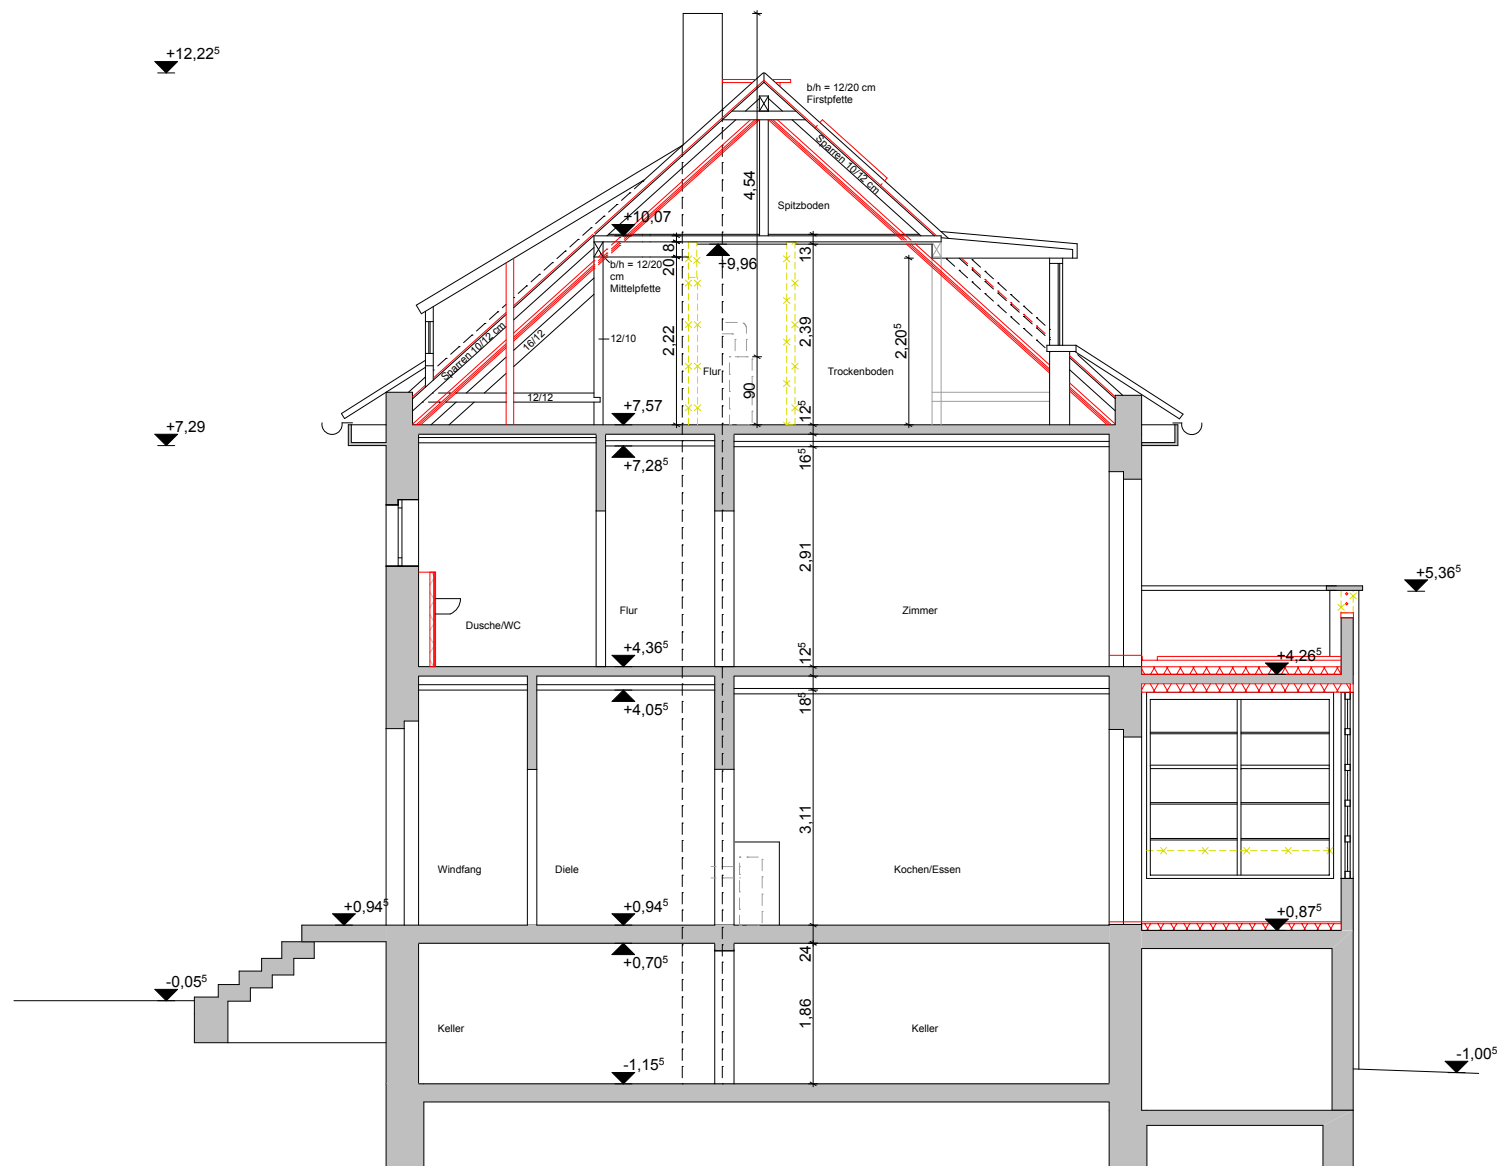

Projekt

Sanierung EFH
Lausicker Str. 26
04299 Leipzig

Architekt

luka architekten
leipzig
Könneritzstraße 25 04229 Leipzig
T 0341 58979071 F 0341 5903337
luka@luka-architekten.de

Bauherr

Fam. Friedlein/ Marius- le- Prince
Breslauer Straße
04299 Leipzig

Leistungsphase

Entwurfsplanung

Plan Nr.

Ist-aes-03

Datum

11.06.2012

Planinhalt

Schnitt

Maßstab

1 : 100



Ansicht von Nordwesten



Ansicht von Südwesten

Projekt	
EFH Fam. Friedlein/ Marius- le- Prince Lausicker Str. 26 04299 Leipzig	
Architekt	
luka architekten leipzig Könneritzstraße 25 04229 Leipzig T 0341 58979071 F 0341 5903337 luka@luka-architekten.de	
Bauherr	
Fam. Friedlein/ Marius- le- Prince Breslauer Straße 04299 Leipzig	
Leistungsphase	
Entwurfsplanung	
Plan Nr.	Datum
Ist-aea-02	11.06.2012
Planinhalt	Maßstab
Ansichten NW/ SW	1 : 100





Ansicht von Südosten





Ansicht von Nordosten



Projekt	
EFH Fam. Friedlein/ Marius- le- Prince Lausicker Str. 26 04299 Leipzig	
Architekt	
luka architekten leipzig Könneritzstraße 25 04229 Leipzig T 0341 58979071 F 0341 5903337 luka@luka-architekten.de	
Bauherr	
Fam. Friedlein/ Marius- le- Prince Breslauer Straße 04299 Leipzig	
Leistungsphase	
Entwurfsplanung	
Plan Nr.	Datum
Ist-ae a-01	11.06.2012
Planinhalt	Maßstab
Ansichten SO/ NO	1 : 100

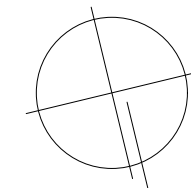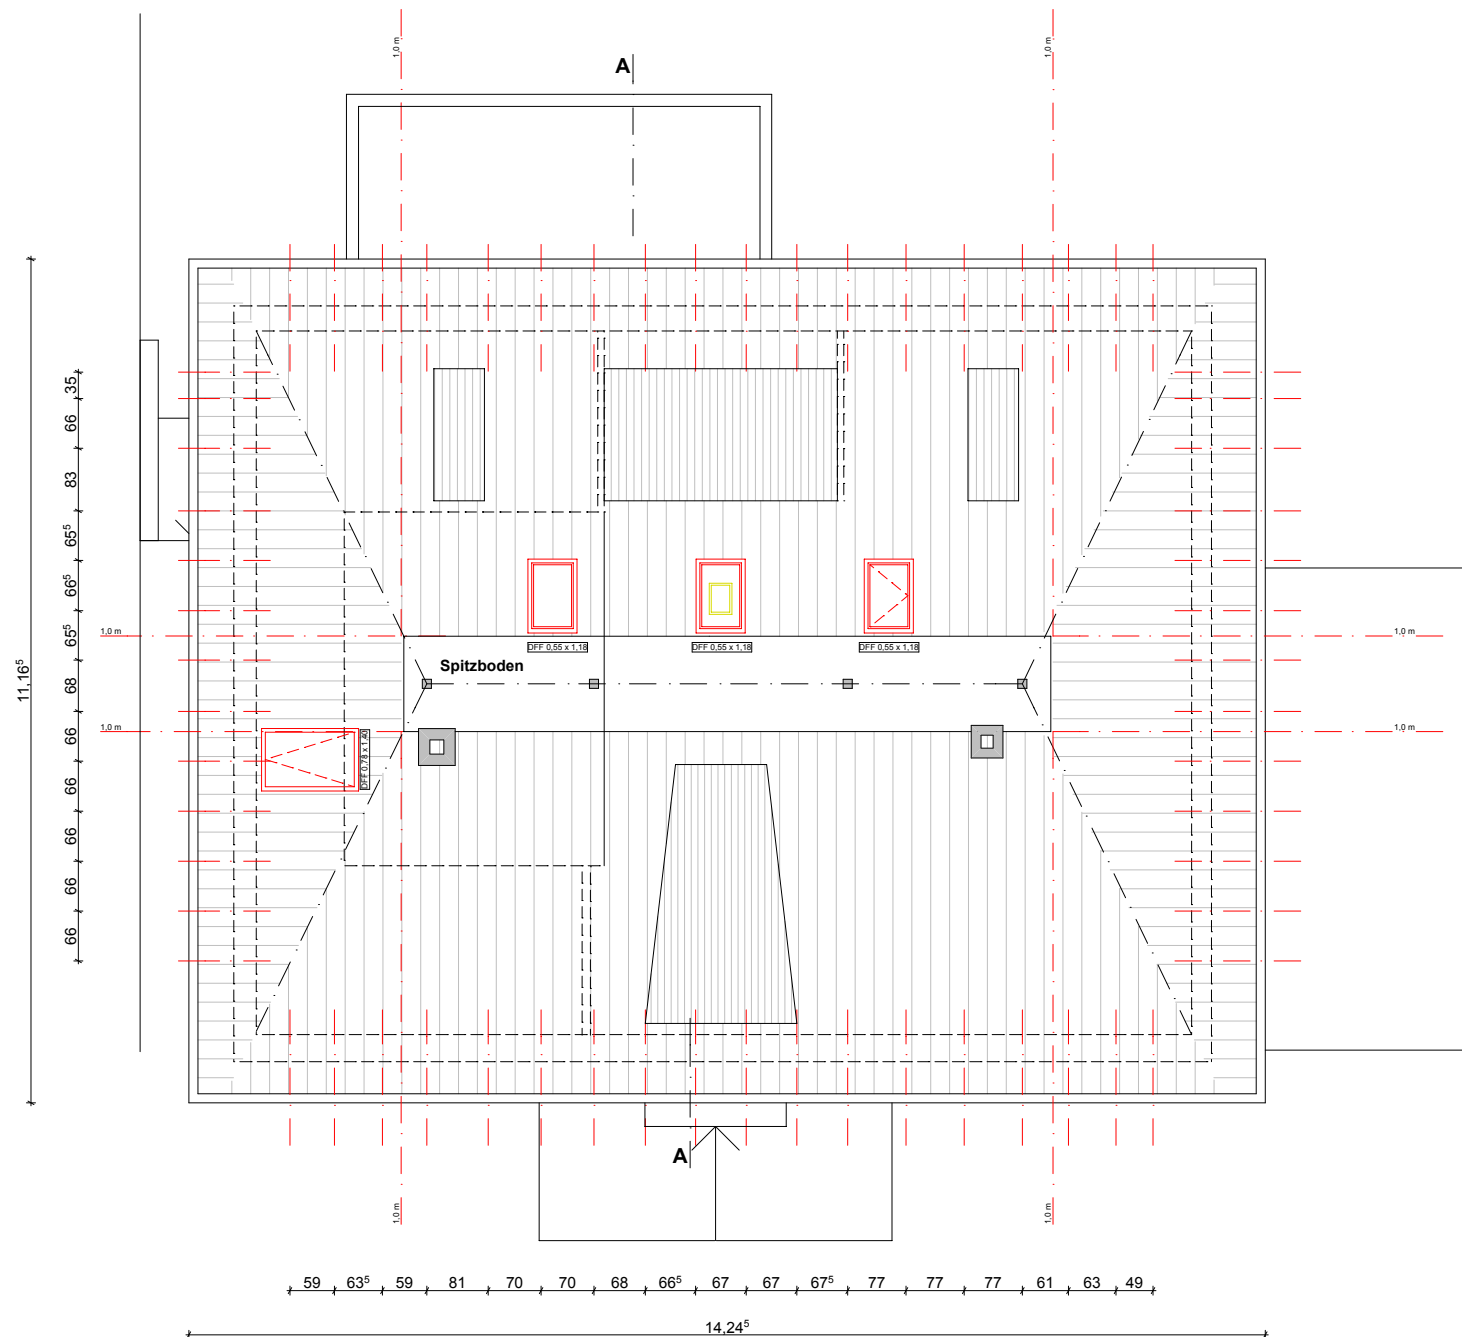


Projekt	
Sanierung EFH Lausicker Str. 26 04299 Leipzig	
Architekt	
luka architekten leipzig Könnertitzstraße 25 04229 Leipzig T 0341 58979071 F 0341 5903337 luka@luka-architekten.de	
Bauherr	
Fam. Friedlein/ Marius- le- Prince Breslauer Straße 04299 Leipzig	
Leistungsphase	
Entwurfsplanung	
Plan Nr. Ist-aeg-08	Datum 11.06.2012
Planinhalt Grundriß Spitzboden	Maßstab 1 : 100

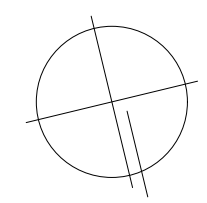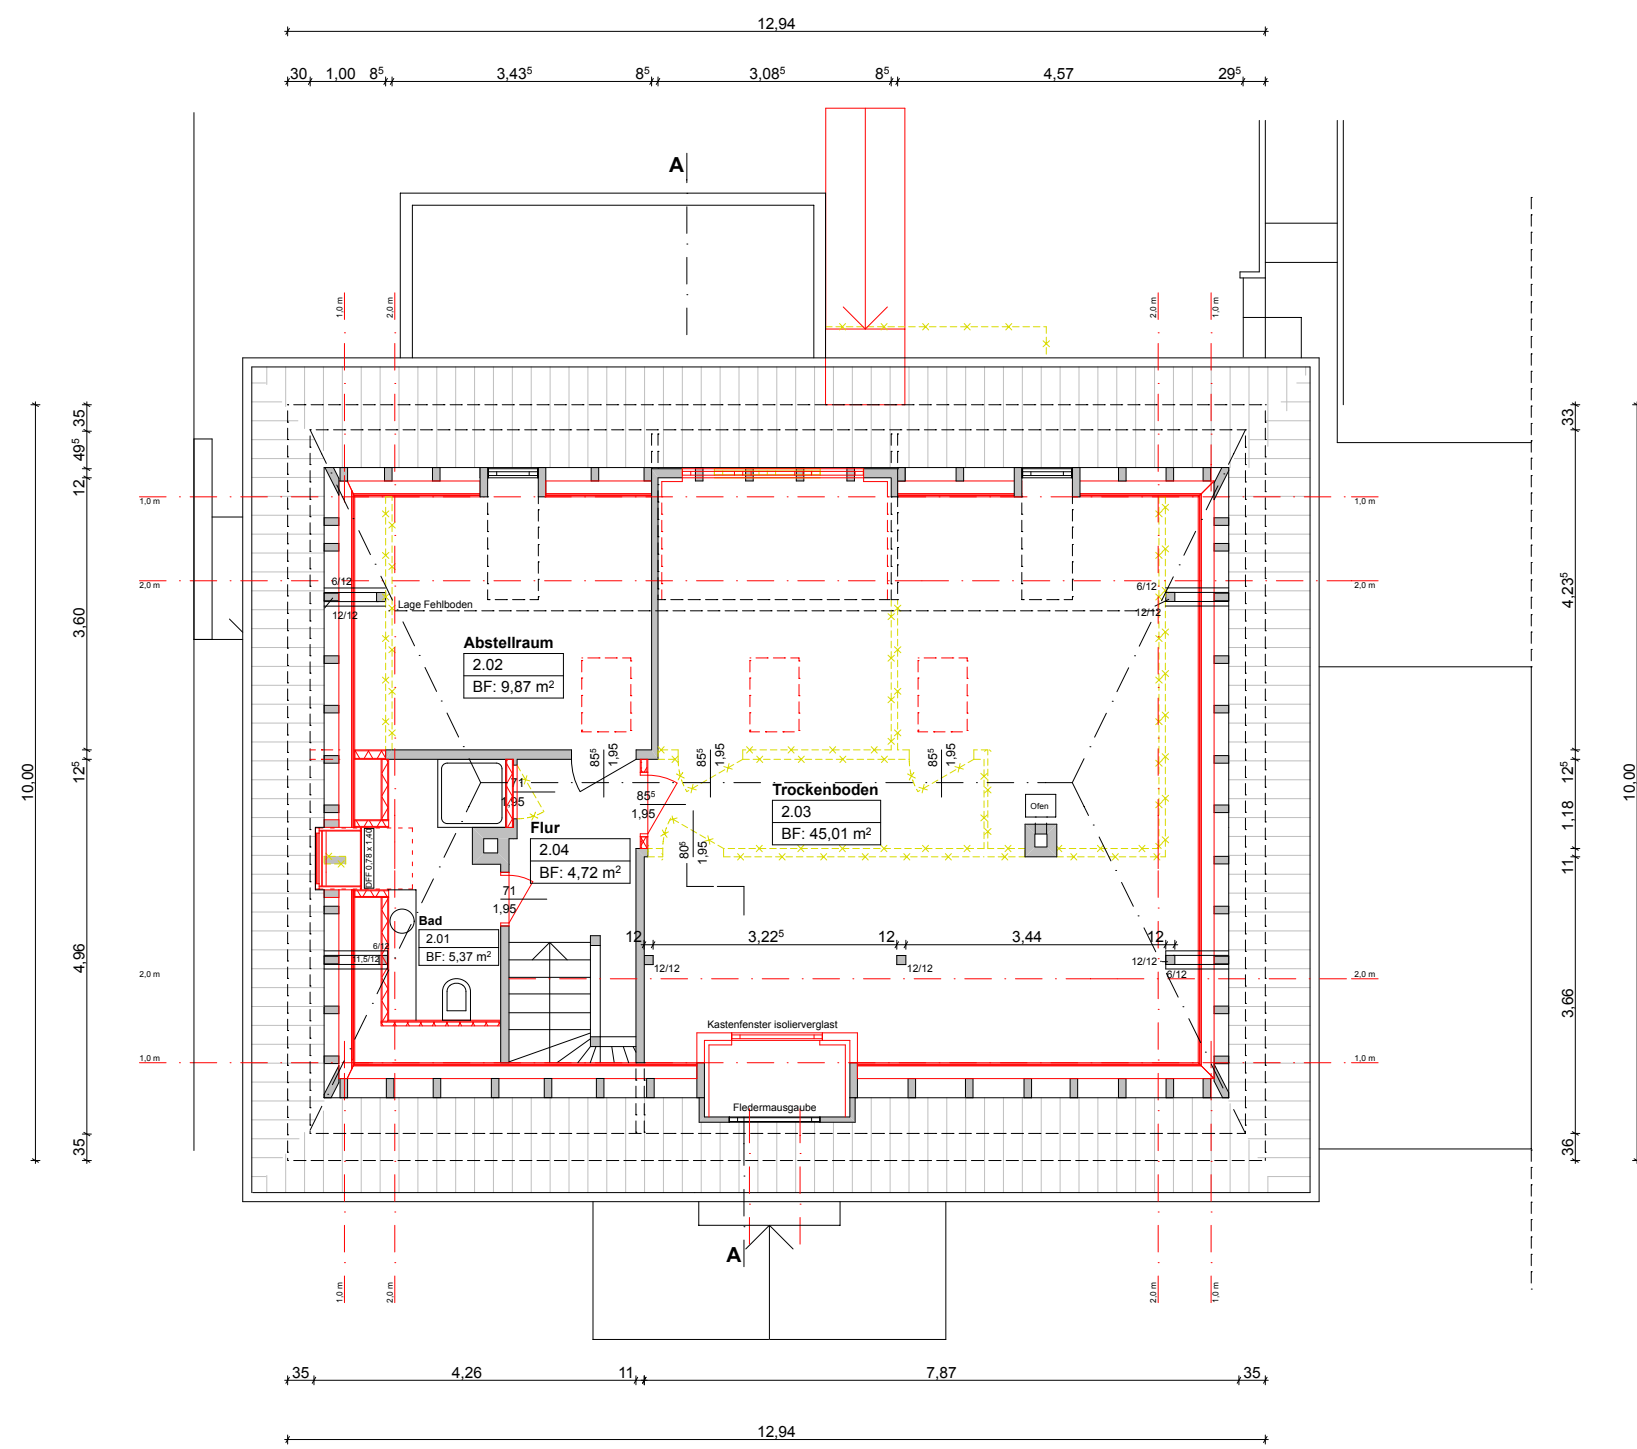

Projekt	
Sanierung EFH Lausicker Str. 26 04299 Leipzig	
Architekt	
luka architekten leipzig Könneritzstraße 25 04229 Leipzig T 0341 58979071 F 0341 5903337 luka@luka-architekten.de	
Bauherr	
Fam. Friedlein/ Marius- le- Prince Breslauer Straße 04299 Leipzig	
Leistungsphase	
Entwurfsplanung	
Plan Nr. Ist-aeg-07	Datum 11.06.2012
Planinhalt Grundriß DG	Maßstab 1 : 100

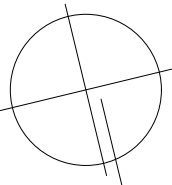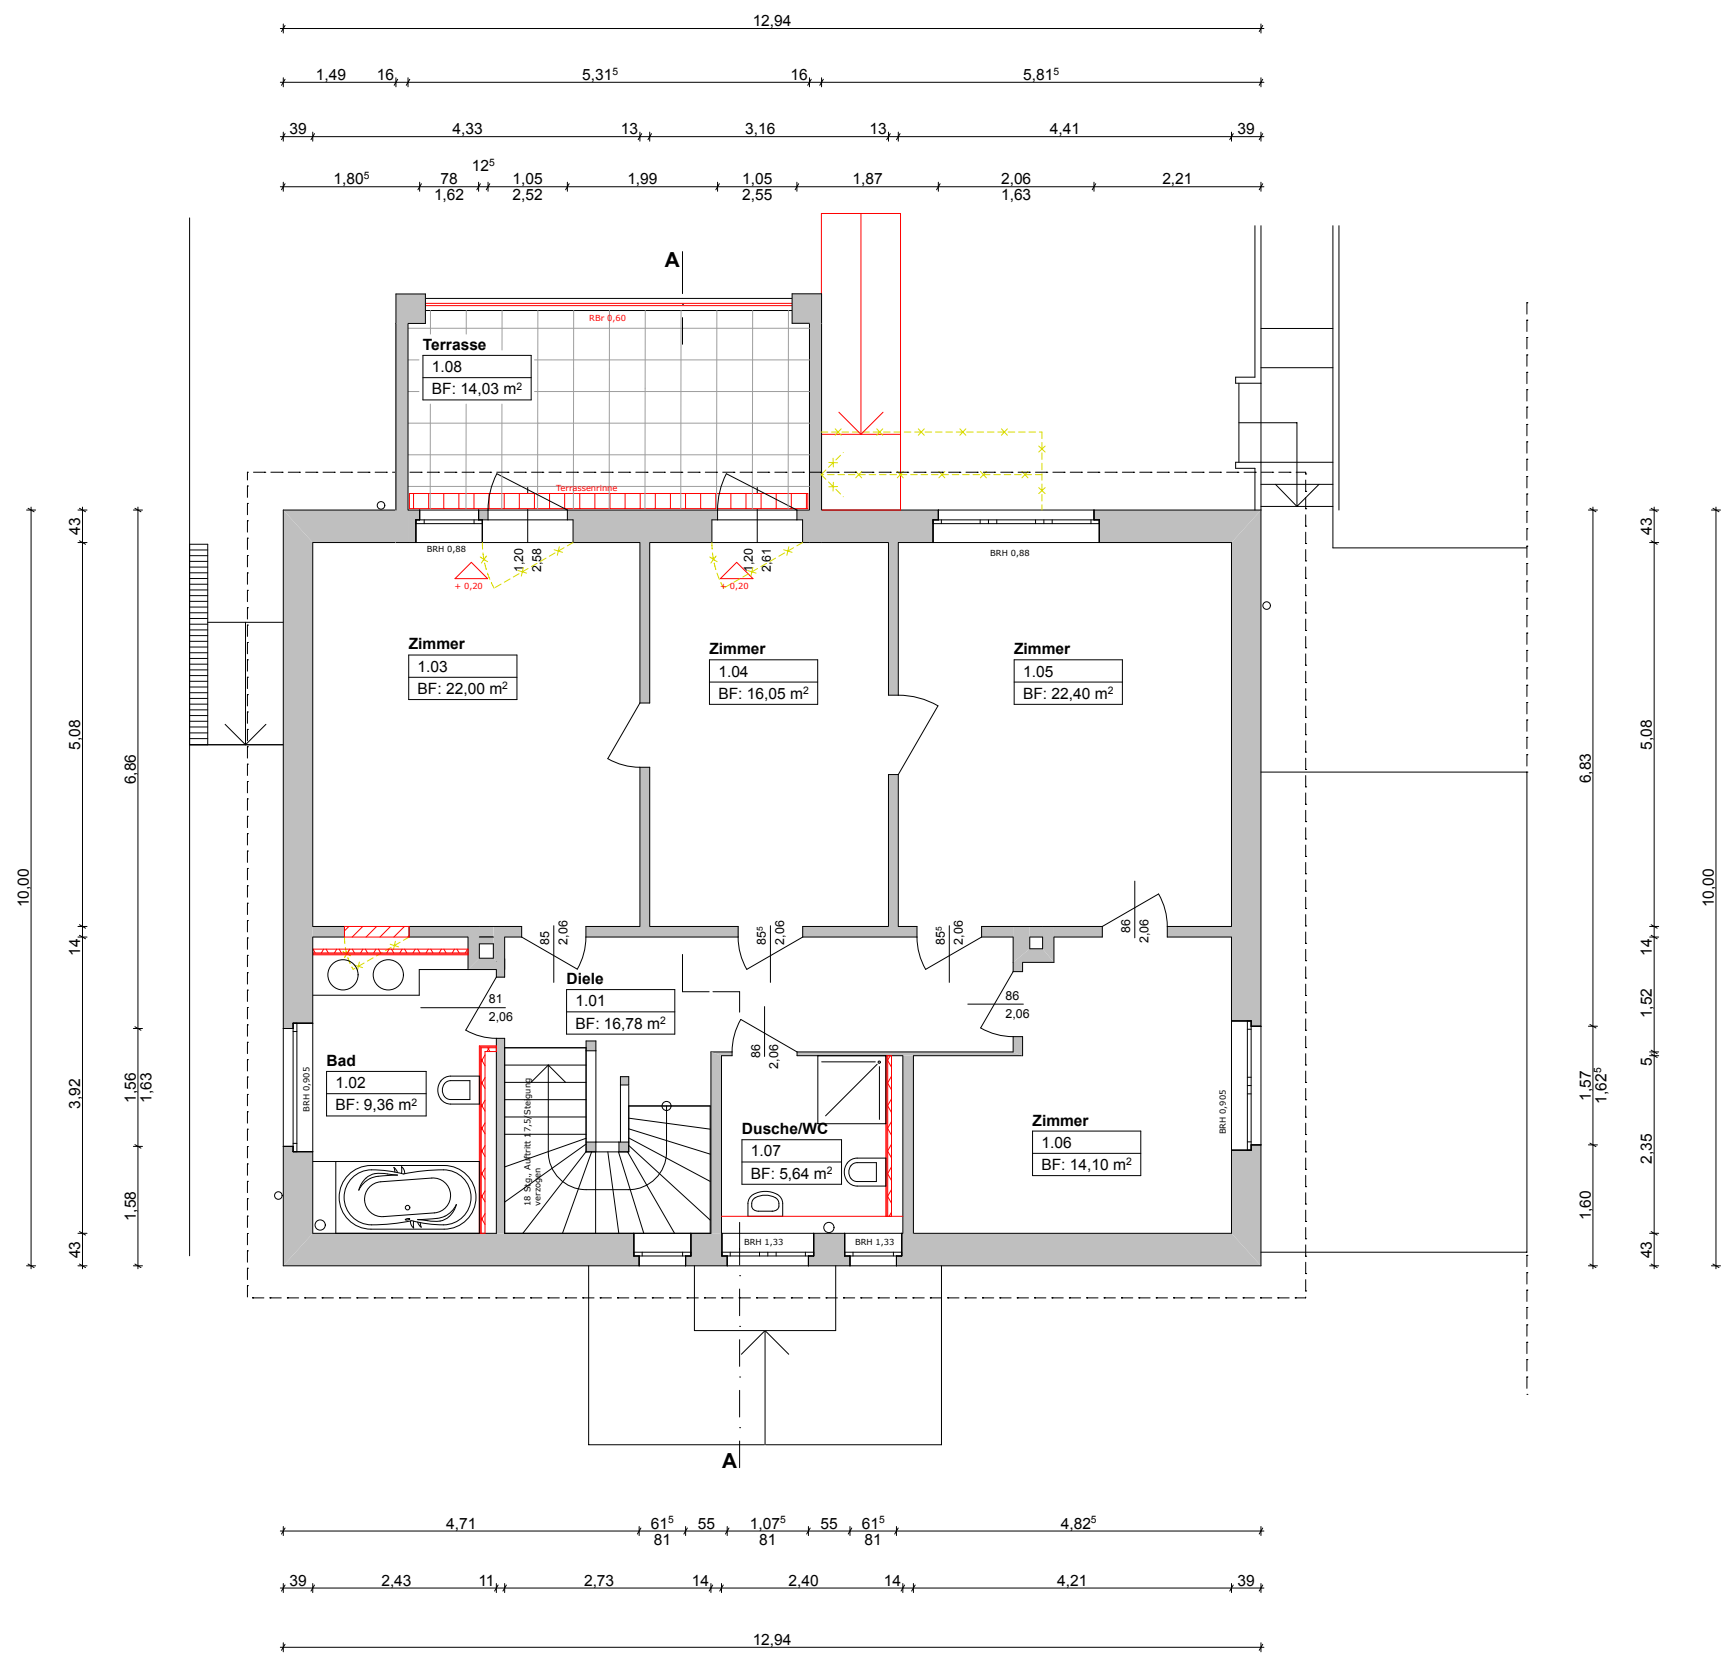

Projekt	
Sanierung EFH Lausicker Str. 26 04299 Leipzig	
Architekt	
luka architekten leipzig Könneritzstraße 25 04229 Leipzig T 0341 58979071 F 0341 5903337 luka@luka-architekten.de	
Bauherr	
Fam. Friedlein/ Marius- le- Prince Breslauer Straße 04299 Leipzig	
Leistungsphase	
Entwurfsplanung	
Plan Nr. Ist-aeg-06	Datum 11.06.2012
Planinhalt Grundriß OG	Maßstab 1 : 100

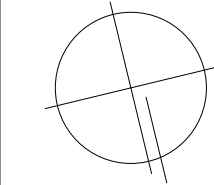

Sanierung EFH
Lausicker Str. 26
04299 Leipzig



luka architekten
leipzig

Könnertitzstraße 25 04229 Leipzig
T 0341 58979071 F 0341 5903337
luka@luka-architekten.de

Fam. Friedlein/ Marius- le- Prince
Breslauer Straße
04299 Leipzig

Entwurfsplanung

Plan Nr. Ist-aeg-05	Datum 11.06.2012
Planinhalt Grundriß EG	Maßstab 1 : 100

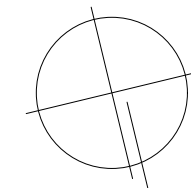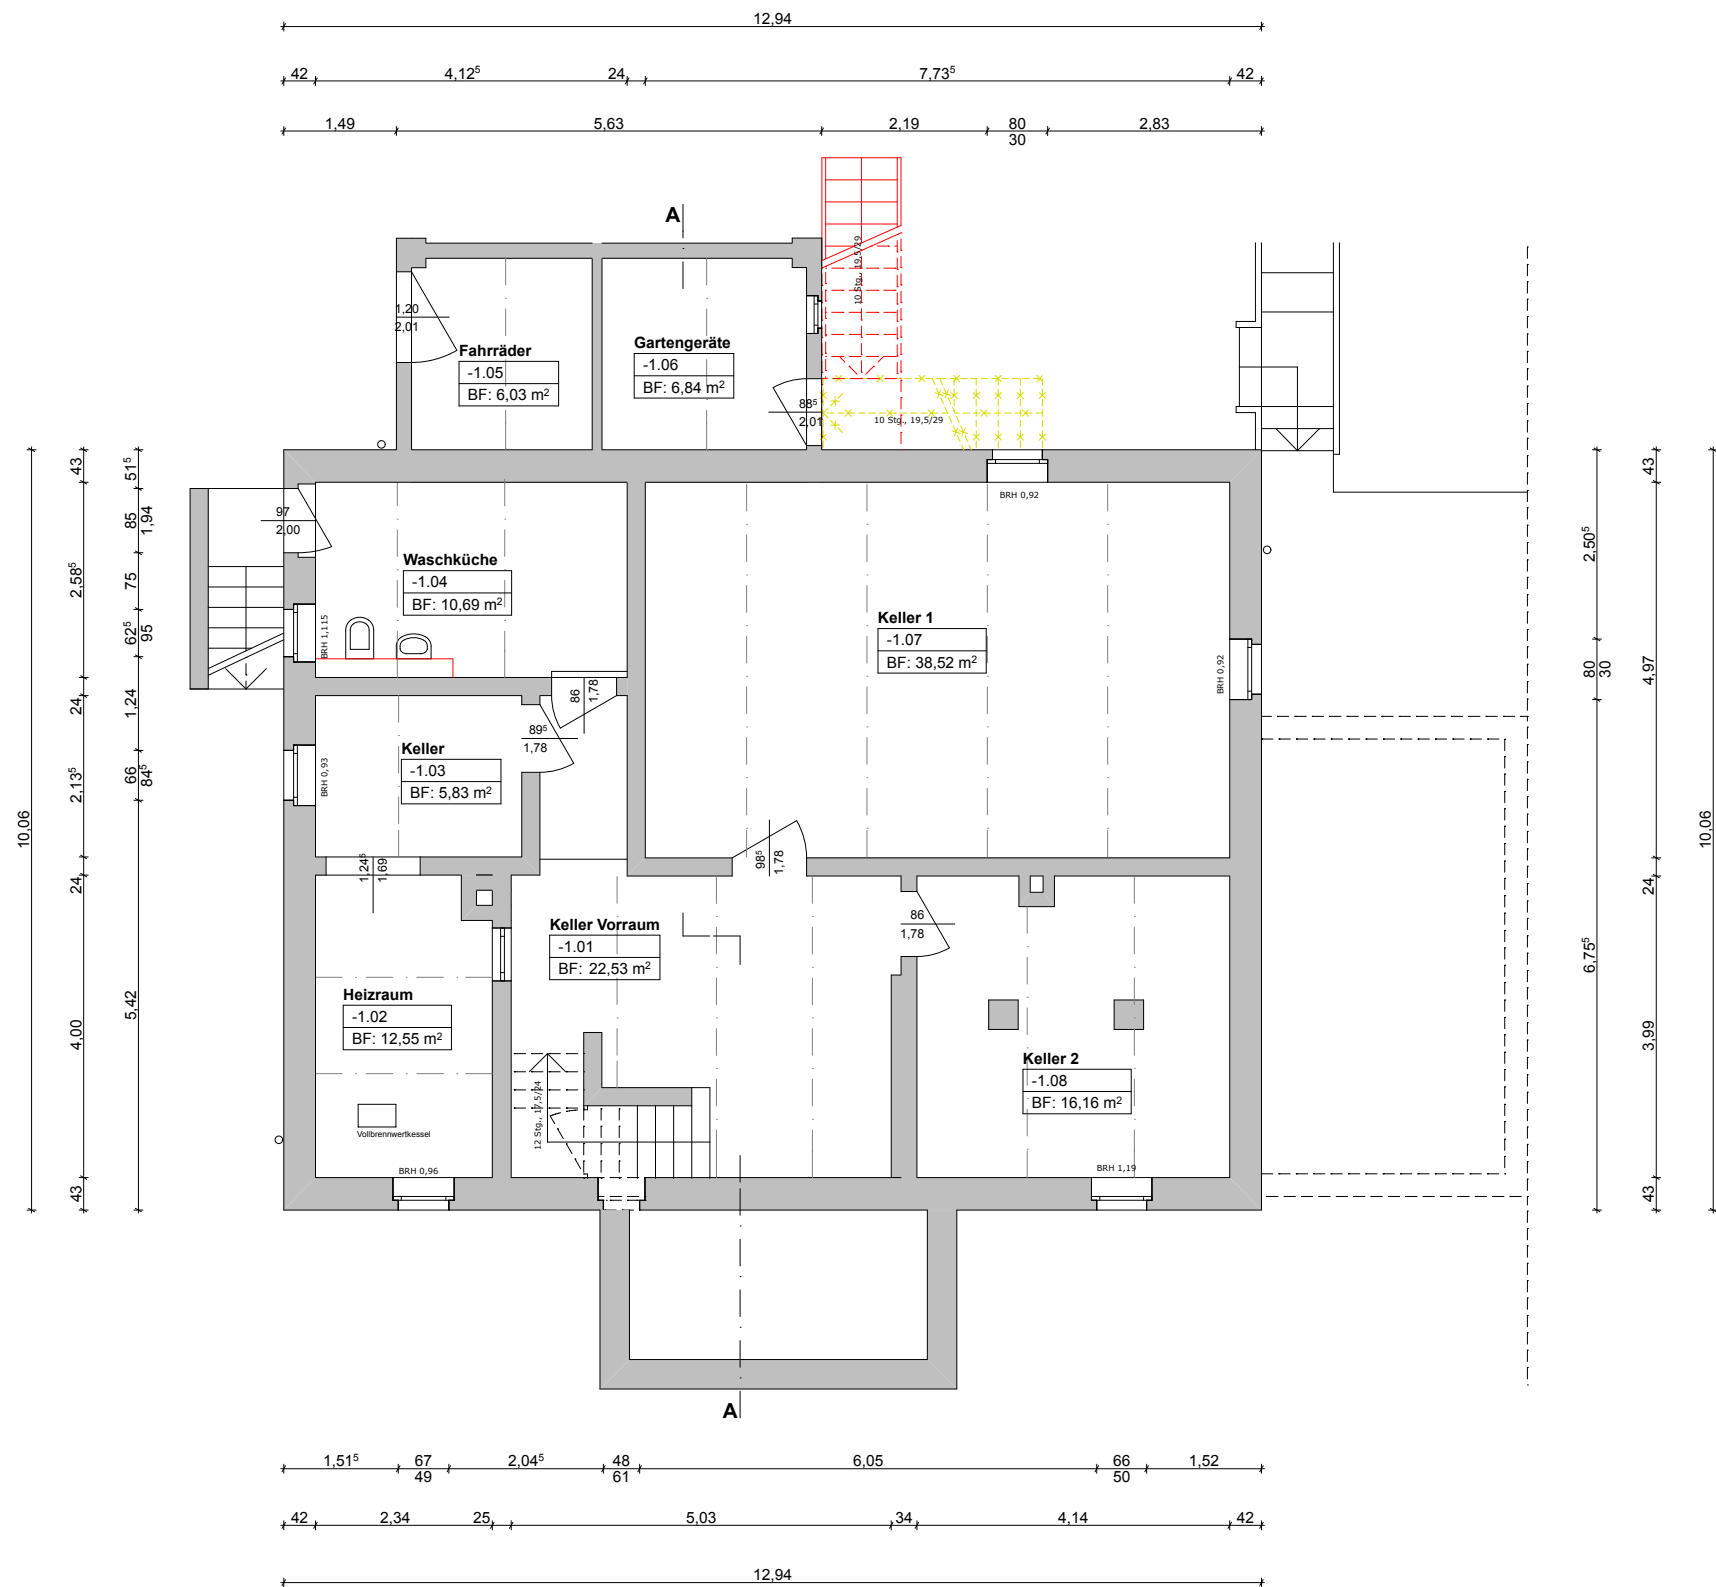

Projekt

Sanierung EFH
Lausicker Str. 26
04299 Leipzig

Architekt

luka architekten
leipzig

Könneritzstraße 25 04229 Leipzig
T 0341 58979071 F 0341 5903337
luka@luka-architekten.de

Bauherr

Fam. Friedlein/ Marius- le- Prince
Breslauer Straße
04299 Leipzig

Leistungsphase

Entwurfsplanung

Plan Nr.

Ist-aeg-04

Datum

11.06.2012

Planinhalt

Grundriß KG

Maßstab

1 : 100