
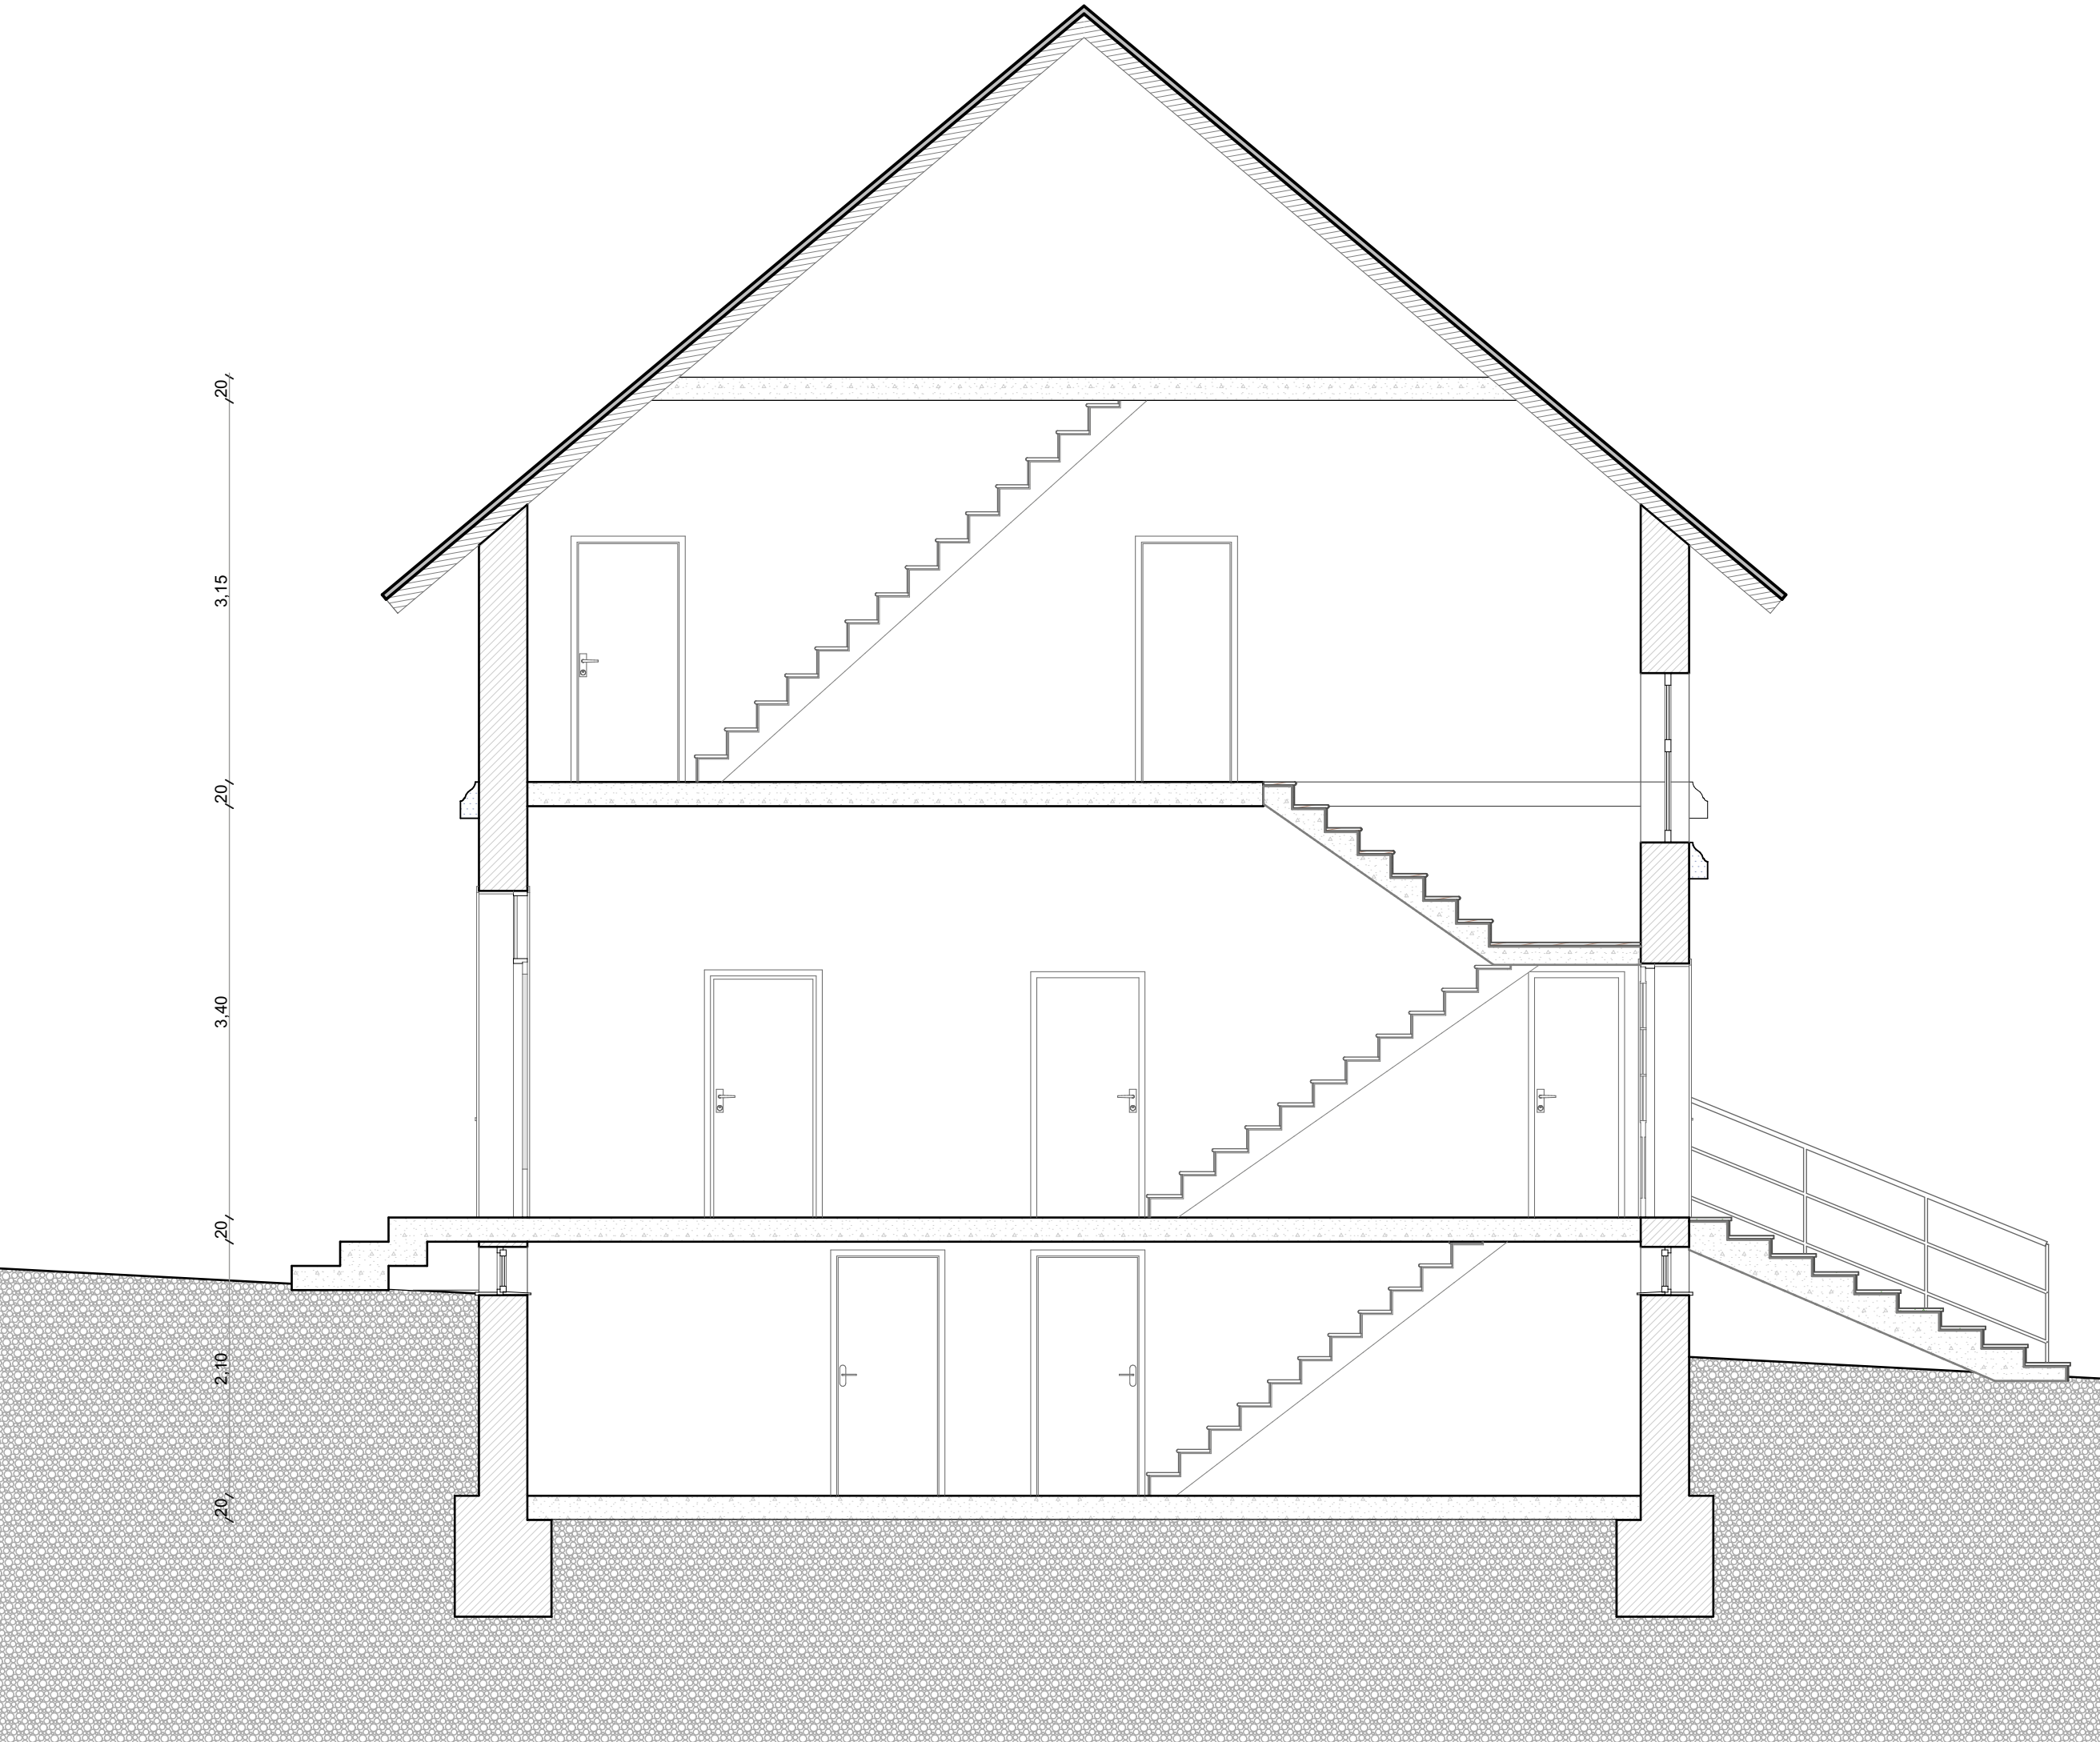


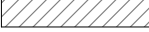

- LEGENDE:
-  Abbruch
  -  Neu
  -  Wände im Bestand

|           |   |         |          |           |
|-----------|---|---------|----------|-----------|
| Projekt   | Neuengammer Hausdeich 256<br>Erneuerung Anbau / Umbau                                                                                  |         |          |           |
| Bauherr   | Finn-Ole Heinrich<br>Neuengammer Hausdeich 256, Hamburg                                                                                |         |          |           |
| Planung   | Rapp + Tochtenhagen Bauplanung GmbH<br>Büro Bornkampsweg 36      22926 Ahrensburg<br>Tel.: 04102 / 45 98 01      Fax: 04102 / 45 98 36 |         |          |           |
| Plantitel | Bestand   |         |          |           |
| Zeichnung | Schnitt S-01   |         |          |           |
| Blatt     | Datum   | Zeichn. | Maßstab  | Blatt Nr. |
|           | 28.08.2019   | JLG.    | M 1 : 50 | 01.5      |